




SCENARIO CABLAGGIO STRUTTURALE

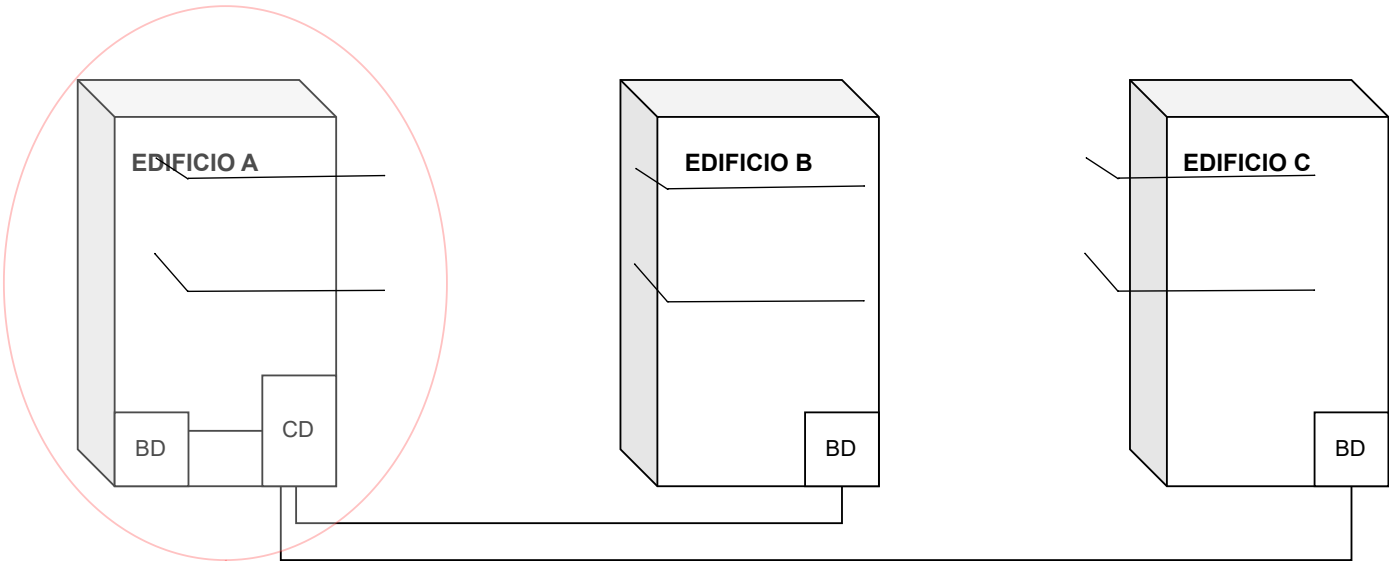

ZOOM EDIFICIO A

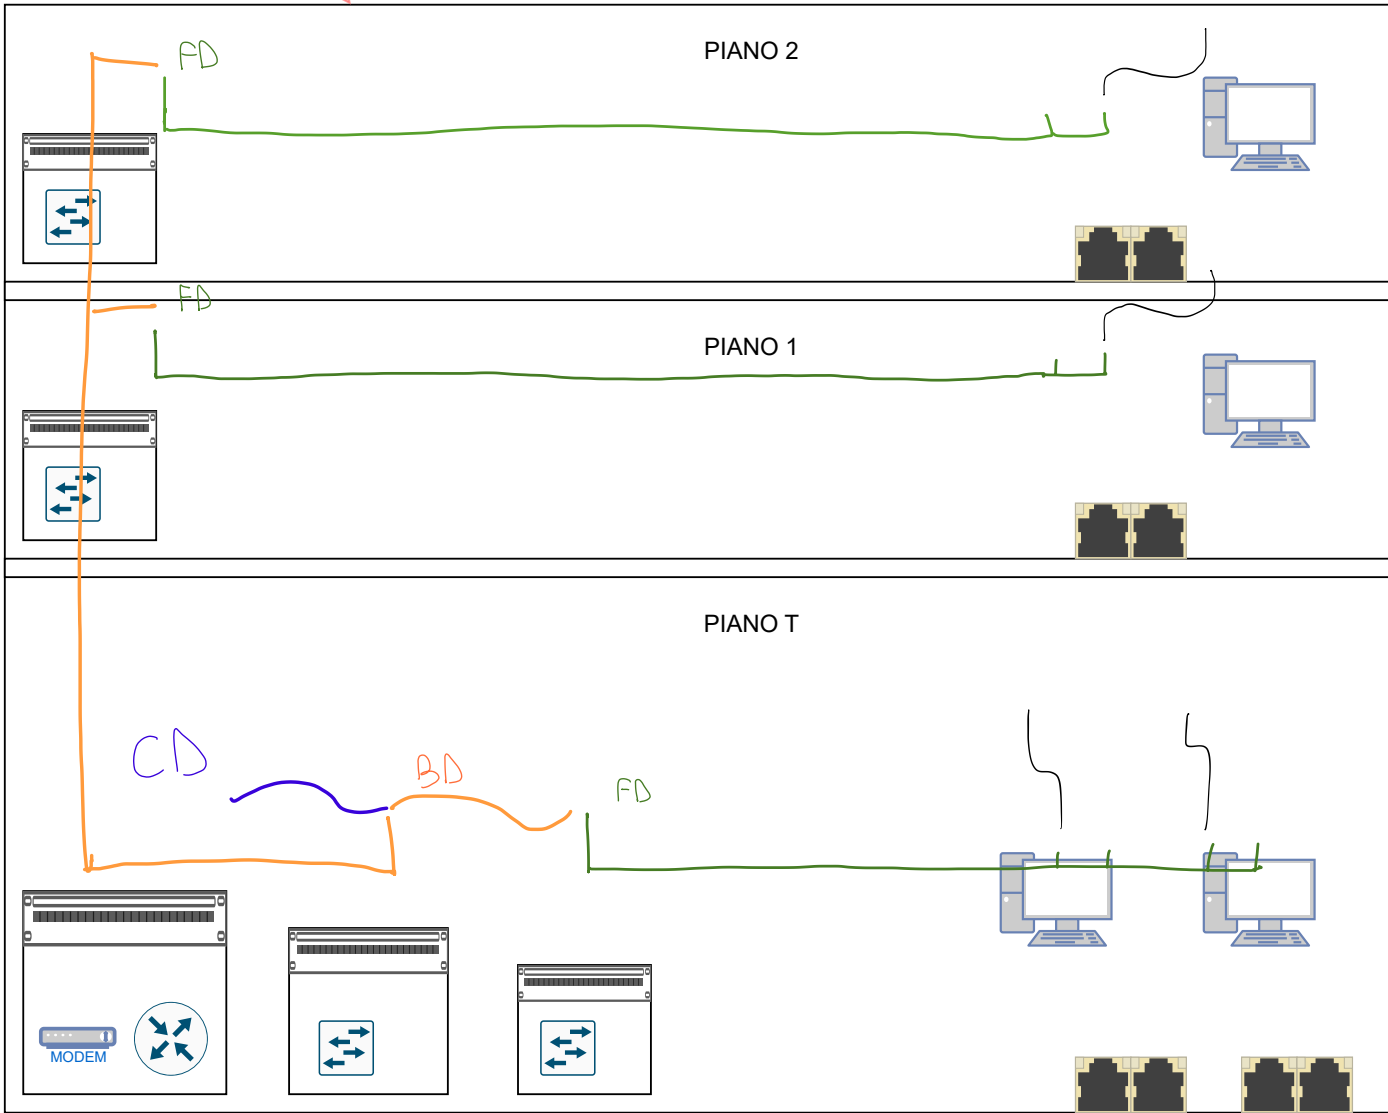

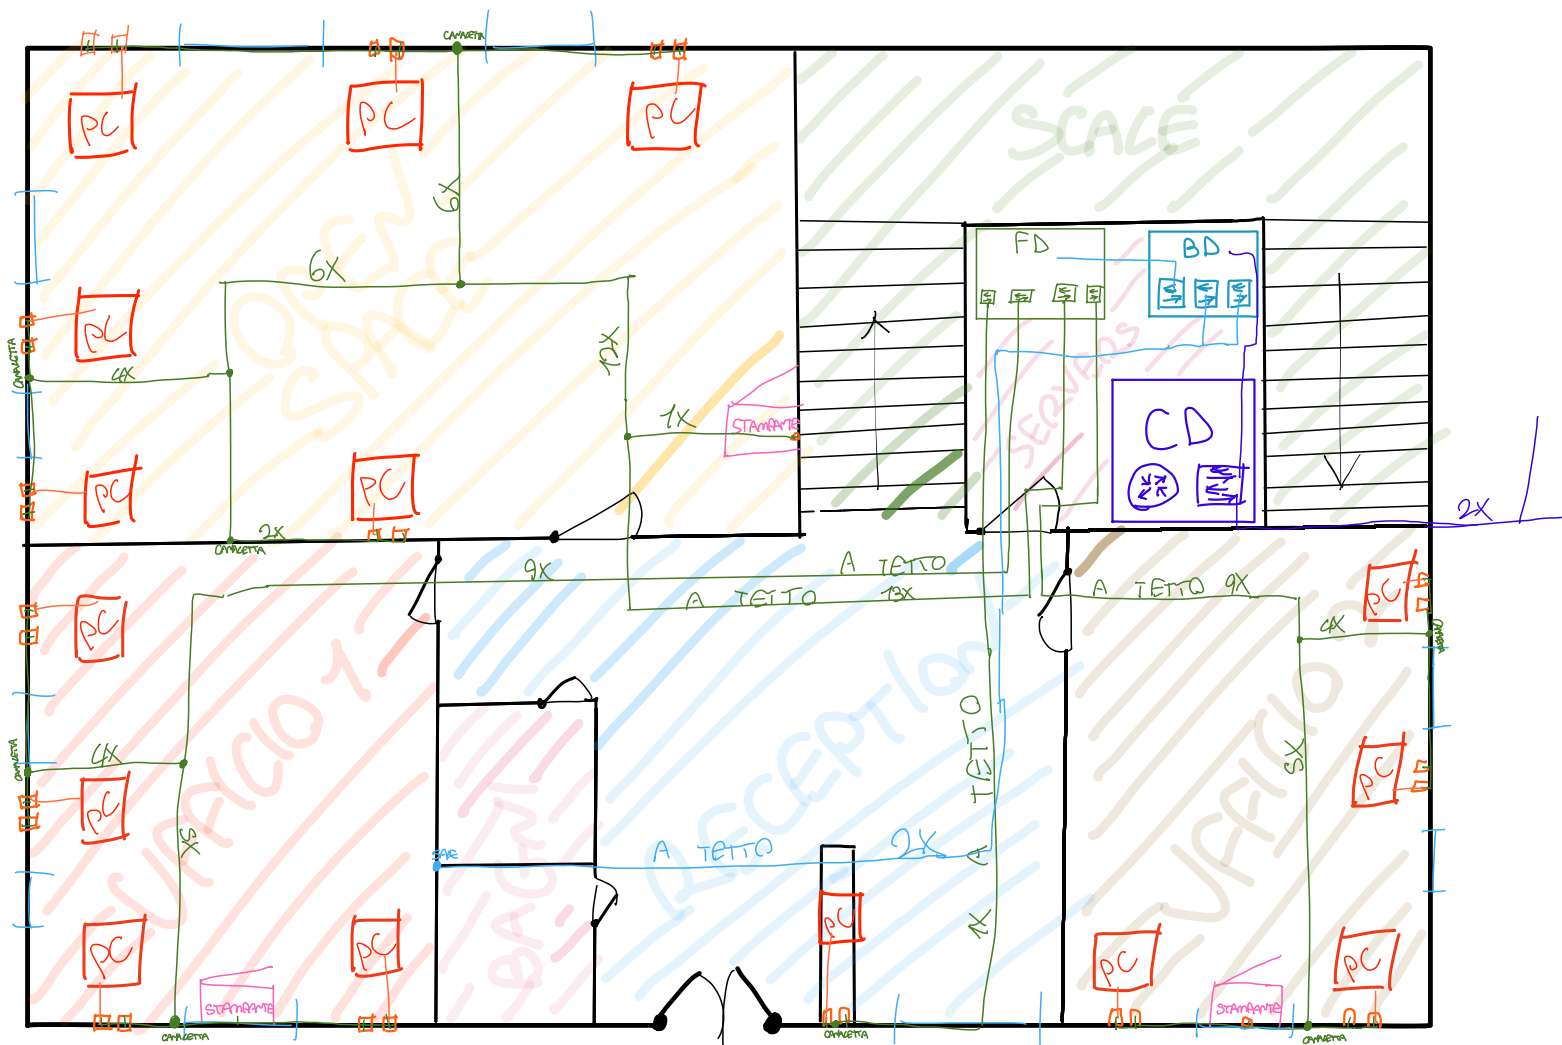

PIANO TERRA